

FIELD NOTES

- ① SEC COR. calculated position from data on survey by J.N. Lentell recorded 1929-Bk. 9 Pg. 84.
- ② NW 1/4 COR. calculated position set at proportional distance ~ see note ① above.
- ③ 1/4 COR. position reestablished from Deed references for R/W from Bliss to P.G.E.E. 1951-Bk. 25, O.R. Pg. 182 Humboldt Co. Records, which describes a 1" iron pipe for 1/4 COR. which was in evidence at that time.
- ④ Found SEC COR. as noted by A.B. Jones in survey rec. 1947-Bk. 11 Pg. 50.
- ⑤ Found NW 1/4 COR. as marked & noted by A.B. Jones in survey rec. 1947-Bk. 11 Pg. 50.
- ⑥ NC 1/4 COR. calculated position ~ see note ① above.
- ⑦ NW 1/4 COR. set 43' easterly on line extended from found NW 1/4 COR. (see note ③ below) 4 ft. 3" N of 4' fir described by Lentell as 1325' easterly from NW 1/4 COR. See J.N. Lentell Survey recorded 1929-Bk. 9 Pg. 84.
- ⑧ Found NW 1/4 COR. as marked & noted by J.N. Lentell in survey recorded 1929-Bk. 9 Pg. 84.
- ⑨ 1/4 COR. calculated position ~ see note ① above.
- ⑩ SW 1/4 COR. calculated position ~ see note ① above.
- ⑪ SW 1/4 COR. position established from 10' stump described by Lentell as BT bearing S42°E, 50' from cor. See J.N. Lentell Survey rec. 1929, Bk. 9, Pg. 84.
- ⑫ 1/4 COR. calculated position from data on Bureau of Land Mgmt. Survey (1960).
- ⑬ Found SEC COR. by R.E. 220 (Frank Kelly) & BCIP dated 1954 as noted on Survey by Bureau of Land Mgmt. (1960).
- ⑭ 1/4 COR. calculated position ~ see note ⑫ above.
- ⑮ SEC COR. position established at Gov't. called distances (3 chains South of Little Larabee Cr.) & at proportional distances between found corners to East & West.
- ⑯ E 1/4 COR. position calculated at proportional distances from Government notes.
- ⑰ 1/4 COR. ~ calculated ~ see note ⑯ above.
- ⑱ W 1/4 COR. ~ calculated ~ see note ⑯ above.
- ⑲ SEC COR. ~ Area logged, cleared & burned over. No sign of BT or OS noted by J.N. Lentell in survey recorded 1929-Bk. 9 Pg. 84. Set 1" iron pipe in mound of rocks. 20 ft. 4" snag bears N34°E, 195' scribed & tagged by LS 2822 (K. Nelson) old face on back side. 18' fir-snag bears S90°E, 13.5' scribed & tagged by LS 2822.
- ⑳ 1/4 COR. calculated position.
- ㉑ 1/4 COR. calculated position ~ see note ⑯ above.
- ㉒ SE 1/4 COR. calculated position ~ see note ⑯ above.
- ㉓ 1/4 COR. calculated position.
- ㉔ 1/4 COR. calculated position.
- ㉕ SEC COR. calculated position based on Sec. Corners described in notes ㉑, ㉒ & ㉓ above: then held Bureau of Land Mgmt. (1960 Survey) distance of South line of Sec. 17 and swung BLM bearing right 01°08' to this map bearing to determine position of Sec. Cor. 17, 18, 19 & 20.

LEGEND

- GOVERNMENT CORNER.
- CORNERS FOUND ON THIS SURVEY.
- ✖ CORNERS CALCULATED ON THIS SURVEY.
- CORNERS ESTABLISHED OR REESTABLISHED ON THIS SURVEY.

FIELD NOTES (continued)

- ㉖ SEC COR. calculated position based on Sec. Corners described in notes ㉕, ㉗ & ㉘ above: then held Bureau of Land Mgmt. (1960 Survey) distance of South line of Sec. 17 and swung BLM bearing right 01°08' to this map bearing to determine position of Sec. Cor. 17, 18, 19 & 20.
- ㉗ 1/4 COR. calculated position.
- ㉘ SEC COR. calculated position based on Sec. Corners described in notes ㉕, ㉗ & ㉙ above: then held Bureau of Land Mgmt. (1960 Survey) distance of South line of Sec. 17 and swung BLM bearing right 01°08' to this map bearing to determine position of Sec. Cor. 17, 18, 19 & 20.

SURVEYOR'S CERTIFICATE

These maps correctly represent a survey made by me in conformance with the requirements of the Land Surveyors' Act at the request of DEERFIELD LTD. in August 1966.

John C. Olson
JOHN. C. OLSON, L.S. 3115



COUNTY SURVEYOR'S CERTIFICATE

These maps have been examined in conformance with the requirements of the Land Surveyors' Act this 29th day of August 1966.

John C. Lentell

County Surveyor



14648 RECORDER'S CERTIFICATE

Recorded at the request of Larson & MacMillan this 2nd day of September 1966 at 4:30 PM, in Book 22 of Surveys at Page(s) 97 flm. 105 Humboldt County Records.

Fee \$21.00

Emma C. Olson
County Recorder, County of Humboldt
State of California

by *Ruth Weston* Deputy

RECORD OF SURVEY

FOR DEERFIELD LTD.


IN SEC. 6, 7, 8, 9, 10, 11, 13, 14, 15, 16, 17, 18, T.I.N., R4E., H.B. & M.
22, 23, 24,
SCALE: 1" = 1000'


AUGUST 1966

LARSON & MACMILLAN
CONSULTING ENGINEERS
EUREKA, CALIF.

SHEET 1 OF 9 SHEETS

BOOK 22 OF SURVEYS PAGE 97

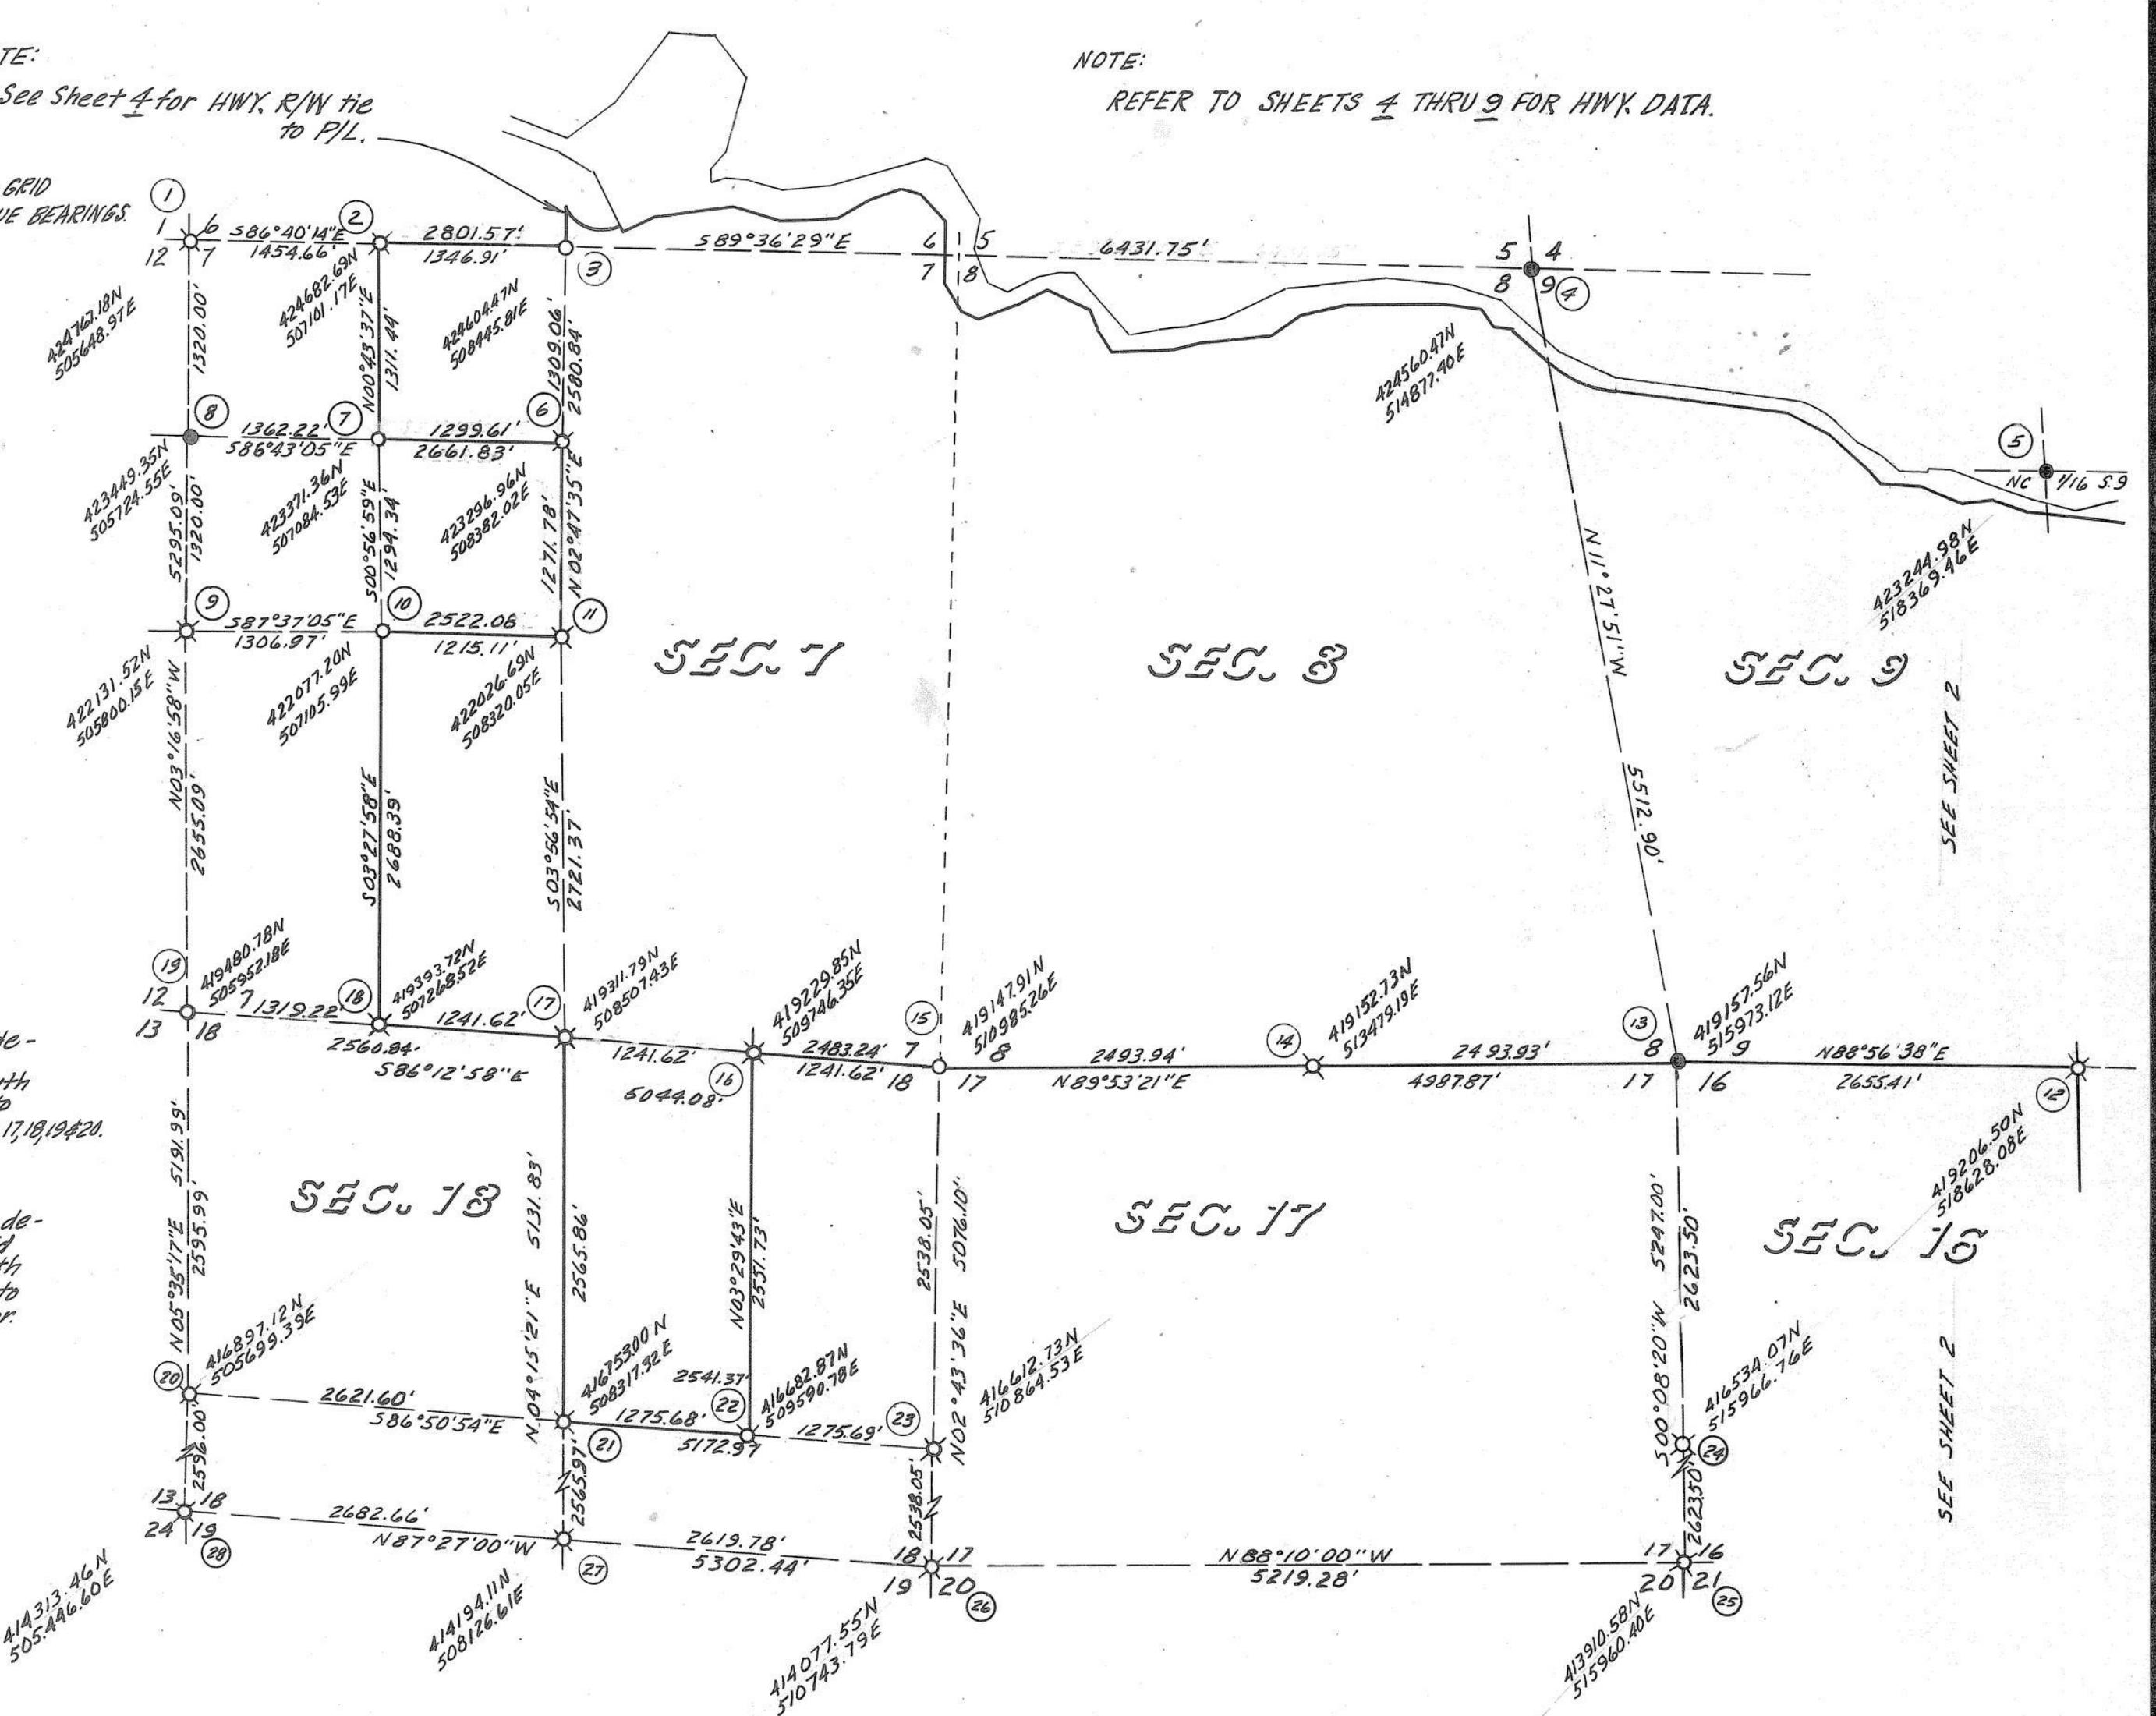

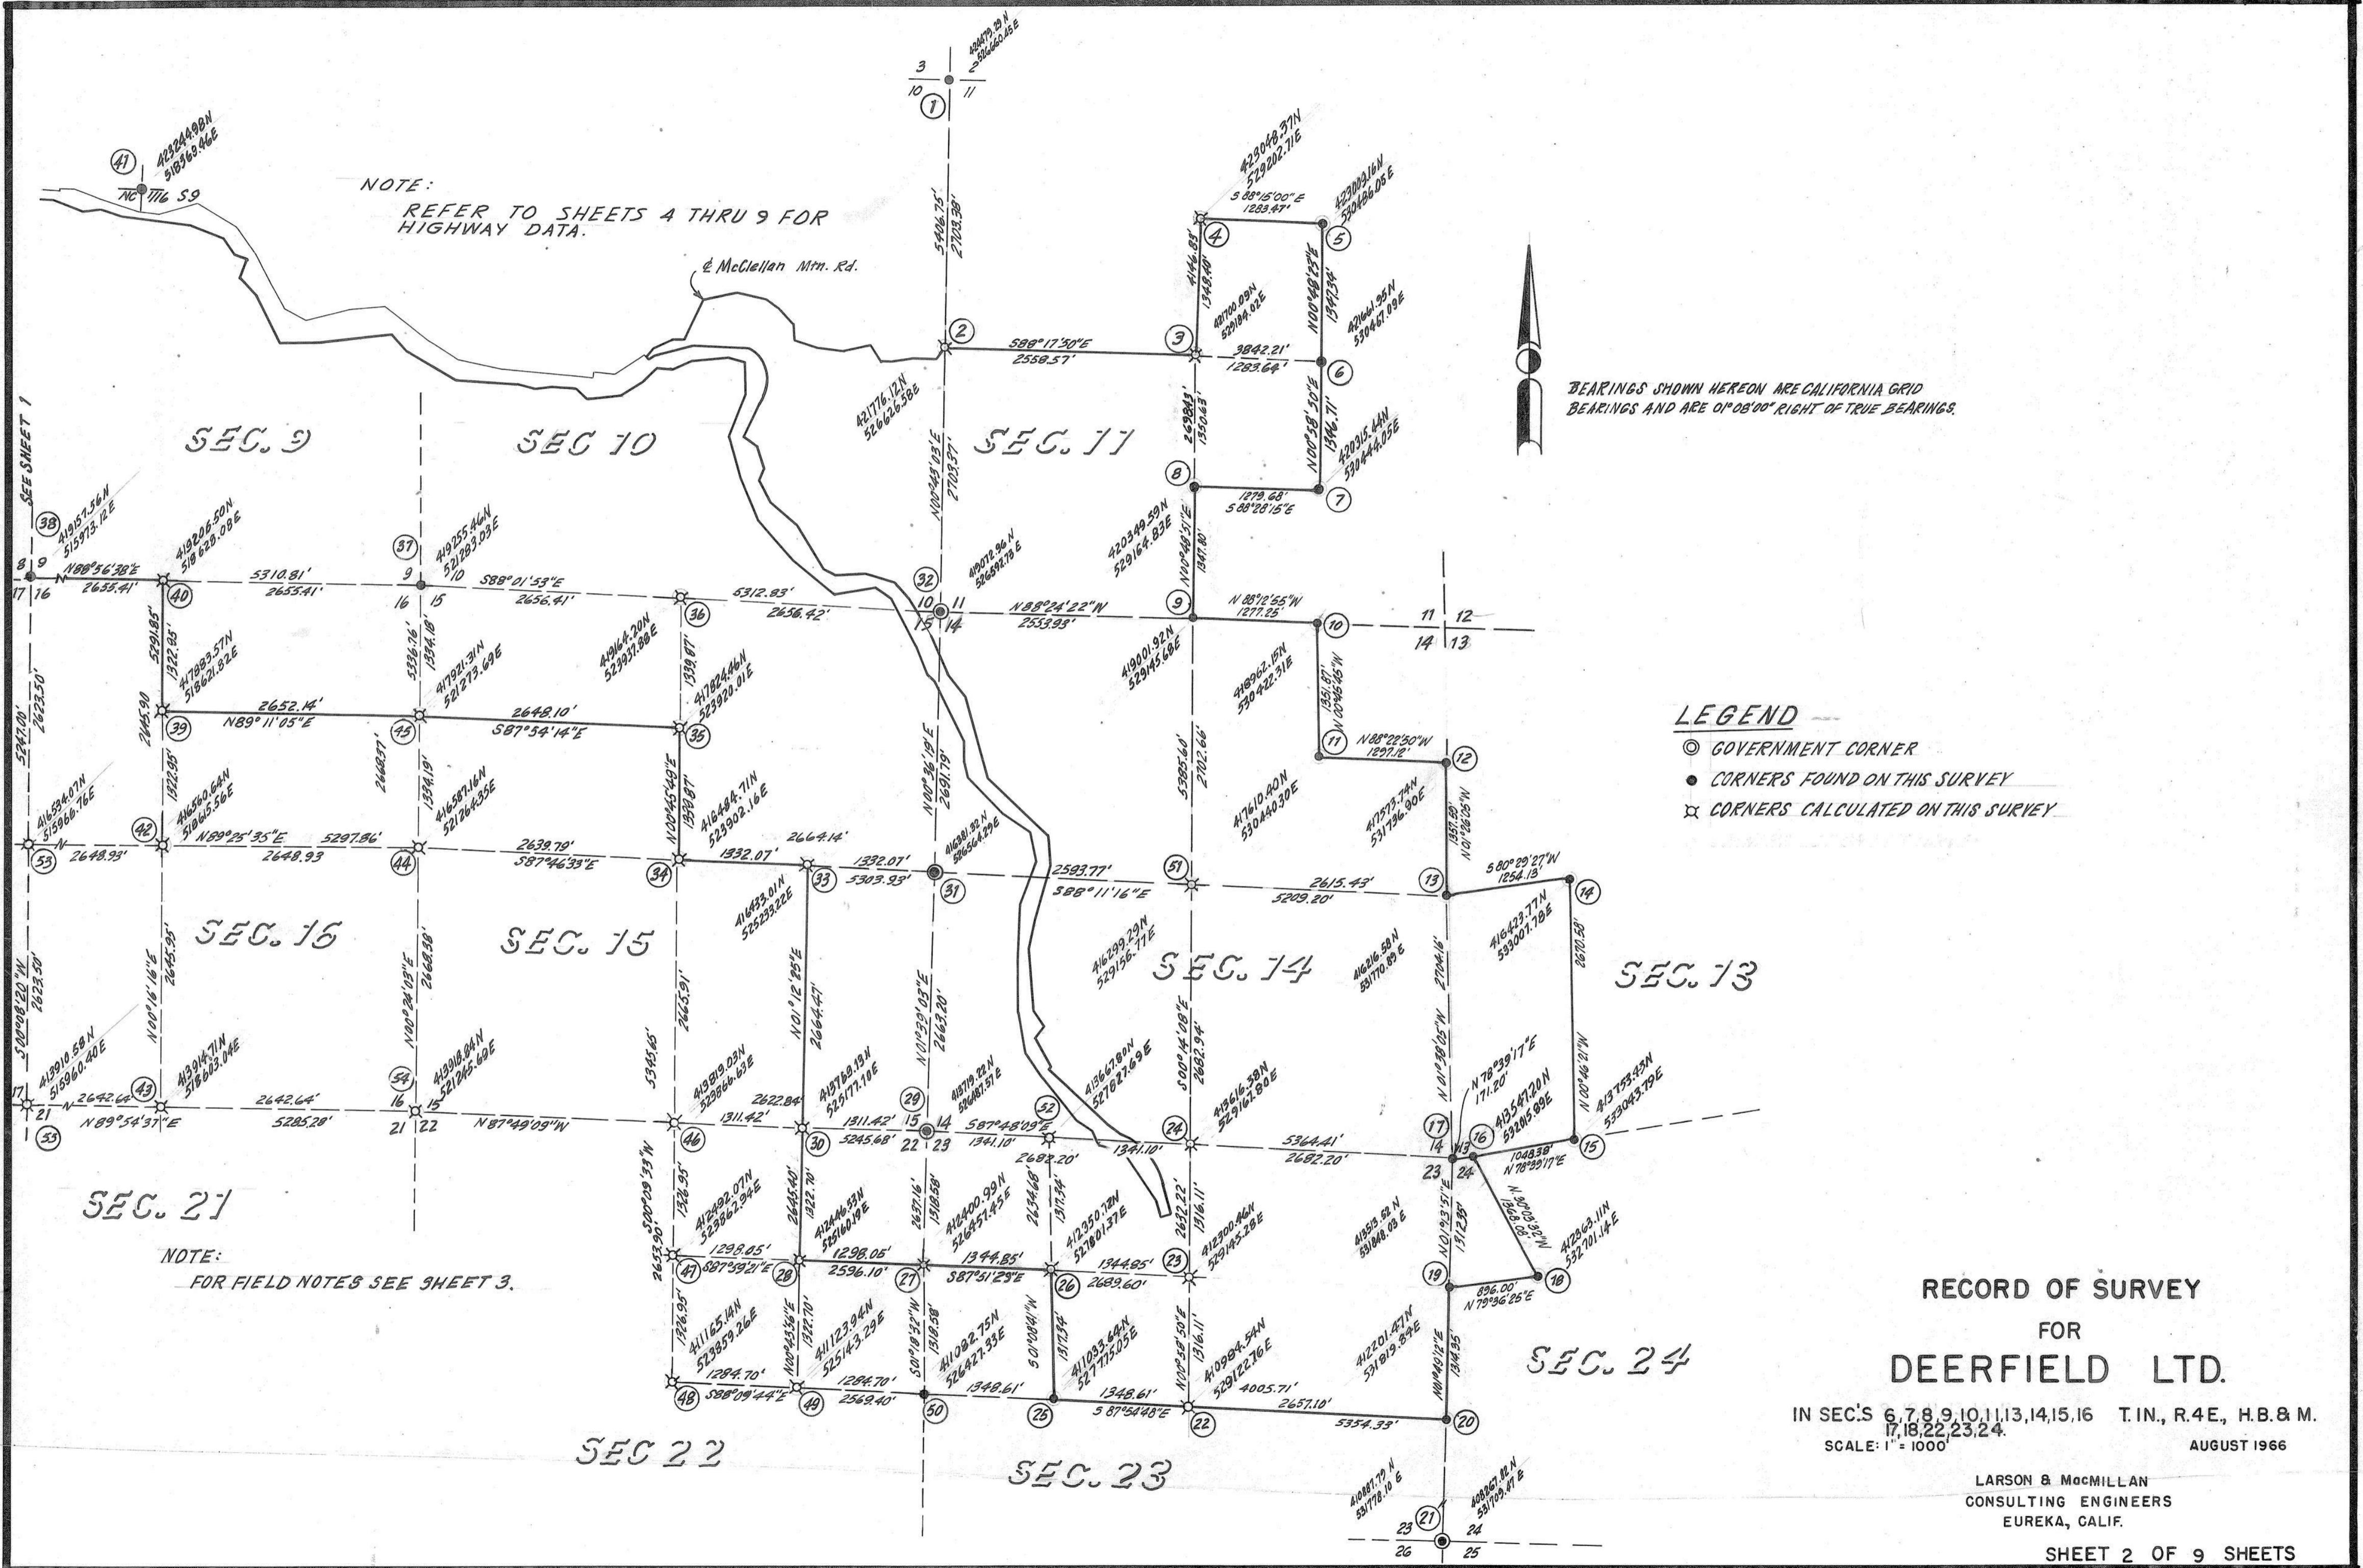

FIELD NOTES - SHEET 2

- (1) Found SEC. COR. set by J.N.Lentell - squared 1/4" Madrone with Roman numeral scribing & tag by LS 2020 (A.B.Bones). 14" Madrone BT bears N 60°W, 4.5' with Roman numeral scribing. 22" Tan Oak BT bears S 30°W, 11.5', corner noted by A.B.Bones in survey recorded 1952 - Bk. 13, Pg. 31.
- (2) 1/4 COR. ~ Corner position calculated from data on survey by A.B.Bones recorded 1952 - Bk. 13, Pg. 31.
- (3) 1/4 COR. ~ corner position calculated - see note (2) above.
- (4) NC 1/16 COR. ~ corner position calculated - see note (2) above.
- (5) Found NE 1/16 COR. as marked & noted by A.B. Bones recorded 1952 - Bk. 13, Pg. 31.
- (6) Found EC 1/16 COR. ~ See note (5) above.
- (7) Found SE 1/16 COR. ~ See note (5) above.
- (8) Found SC 1/16 COR. ~ See note (5) above.
- (9) Found 1/4 COR. ~ See note (5) above.
- (10) Found E 1/16 COR. ~ See note (5) above - & as noted by O.G. Larson in survey recorded 1957 - Bk. 15, Pg. 130.
- (11) Found NE 1/16 COR. ~ see note (5) above.
- (12) Found N 1/16 COR. ~ see note (5) & (10) above.
- (13) Found 1/4 COR. ~ see note (5) & (10) above.
- (14) Found WC 1/16 COR. as marked & noted by O.G. Larson in survey recorded 1957 - Bk. 15, Pg. 130.
- (15) Found W 1/16 COR. ~ see note 14 above - & as noted by H.I. Bower in survey recorded 1958 - Bk. 16, Pg. 85.
- (16) Found BT only (no pipe) as noted for PROPERTY CORNER by H.I. Bower in survey recorded 1958 - Bk. 16, Pg. 85. 16" White Oak bears S 86°42'E, 68.2'.
- (17) Found SEC. COR. ~ see notes (2) & (15) above.
- (18) Found BT only (no pipe) as noted for PROPERTY CORNER by H.I. Bower in Survey recorded 1958 - Bk. 16, Pg. 85. 16" White Oak bears S 17°14'E, 60'.
- (19) Found N 1/16 COR. as marked & noted by H.I. Bower in survey recorded 1958 - Bk. 16, Pg. 85.
- (20) Found 1/4 COR. ~ see note (19) above.
- (21) Found GOV'T. SEC. COR. as marked & noted by J.N.Lentell in survey recorded 1914 - Bk. 6, Pg. 45, & as noted by H.I.Bower in survey recorded 1958 - Bk. 16, Pg. 85.
- (22) C 1/4 COR. calculated position from data on survey by H.I. Bower recorded 1958 - Bk. 16, Pg. 85.
- (23) NC 1/16 COR. calculated - see note (22) above.
- (24) 1/4 COR. calculated - see note (22) above.
- (25) Found WC 1/16 COR. ~ see note (22) above.
- (26) NW 1/16 COR. calculated position from data on survey by H.I. Bower recorded 1958 - Bk. 16, Pg. 85.
- (27) N 1/16 COR. calculated position - see note (22) above.
- (28) NE 1/16 COR. calculated - see note (22) above.
- (29) Found GOV'T. SEC. COR. noted by J.N.Lentell in survey recorded 1914 - Bk. 6, Pg. 45 & H.I. Bower in survey recorded 1958 - Bk. 16, Pg. 85.
- (30) E 1/16 COR. ~ calculated - see note (26) above.
- (31) GOV'T. 1/4 COR. noted by J.N.Lentell in survey recorded 1921 - Bk. 8, Pg. 50.
- (32) Found GOV'T. SEC. COR. as noted by J.N.Lentell in survey recorded 1914 - Bk. 6, Pg. 45 & as noted by A.B.Bones in survey recorded 1952 - Bk. 13, Pg. 31.
- (33) EC 1/16 COR. calculated position from data on Bureau of Land Mgmt. Survey dated 1960.
- (34) C 1/4 COR. calculated position - see note (33) above.
- (35) NC 1/16 COR. calculated position - see note (33) above.
- (36) 1/4 COR. calculated position - see note (33) above.
- (37) Found SEC. COR. as marked & noted in Bureau of Land Mgmt. Survey, dated 1960.
- (38) Found SEC. COR. by RE 220 (Frank Kelly) & BCIP dated 1954 as noted in Bureau of Land Mgmt. Survey 1960.
- (39) NC 1/16 COR. calculated position - see note (33) above.
- (40) 1/4 COR. calculated position - see note (33) above.
- (41) Found NC 1/16 COR. as marked & noted by A.B. Bones in survey recorded 1947 - Bk. 11, Pg. 150.
- (42) C 1/4 COR. calculated - see note (33) above.
- (43) 1/4 COR. calculated - see note (33) above.
- (44) 1/4 COR. calculated - see note (33) above.
- (45) N 1/16 COR. calculated - see note (33) above.
- (46) 1/4 COR. ~ calculated - see note (33) above.
- (47) NC 1/16 COR. ~ calculated - see note (33) above.
- (48) C 1/4 COR. ~ calculated - see note (33) above.
- (49) EC 1/16 COR. ~ calculated - see note (33) above.
- (50) Found C 1/4 COR. ~ Bureau of Land Mgmt. BCIP dated 1954. 12" OAK BT bears S 21°W, 31.5' with BLM tag. 10" OAK BT bears S 72°W, 10' with BLM tag.
- (51) C 1/4 COR. calculated position from data on survey by J.N.Lentell recorded 1921 - Bk. 8, Pg. 50.
- (52) W 1/16 COR. calculated position - see note (26) above.
- (53) C 1/4 COR. calculated position - see note (33) above.
- (54) SEC. COR. calculated position based on found Sec. Corners described in notes (29), (32) & (37) above, then held Bureau of Land Mgmt. (1960 survey) distance on South & West Sec. lines of Sec. 15 to determine position of Sec. Cor. 15, 16, 21 & 22.
- (55) SEC. COR. calculated position based on Sec. Corners described in notes (30), (38) & (34) above: then held Bureau of Land Mgmt. (1960 survey) distance on South & West Sec. lines of Sec. 16 to determine position of Sec. Corner 16, 17, 20 & 21.

RECORD OF SURVEY FOR DEERFIELD LTD.


IN SEC'S. 6,7,8,9,10,11,13,14,15,16,17, T.I.N., R.4 E., H.B.8 M.
18,22,23,24.


AUGUST 1966


LARSON & MACMILLAN
CONSULTING ENGINEERS
EUREKA, CALIF.

SHEET 3 OF 9 SHEETS

BOOK 22 OF SURVEYS, PAGE 99

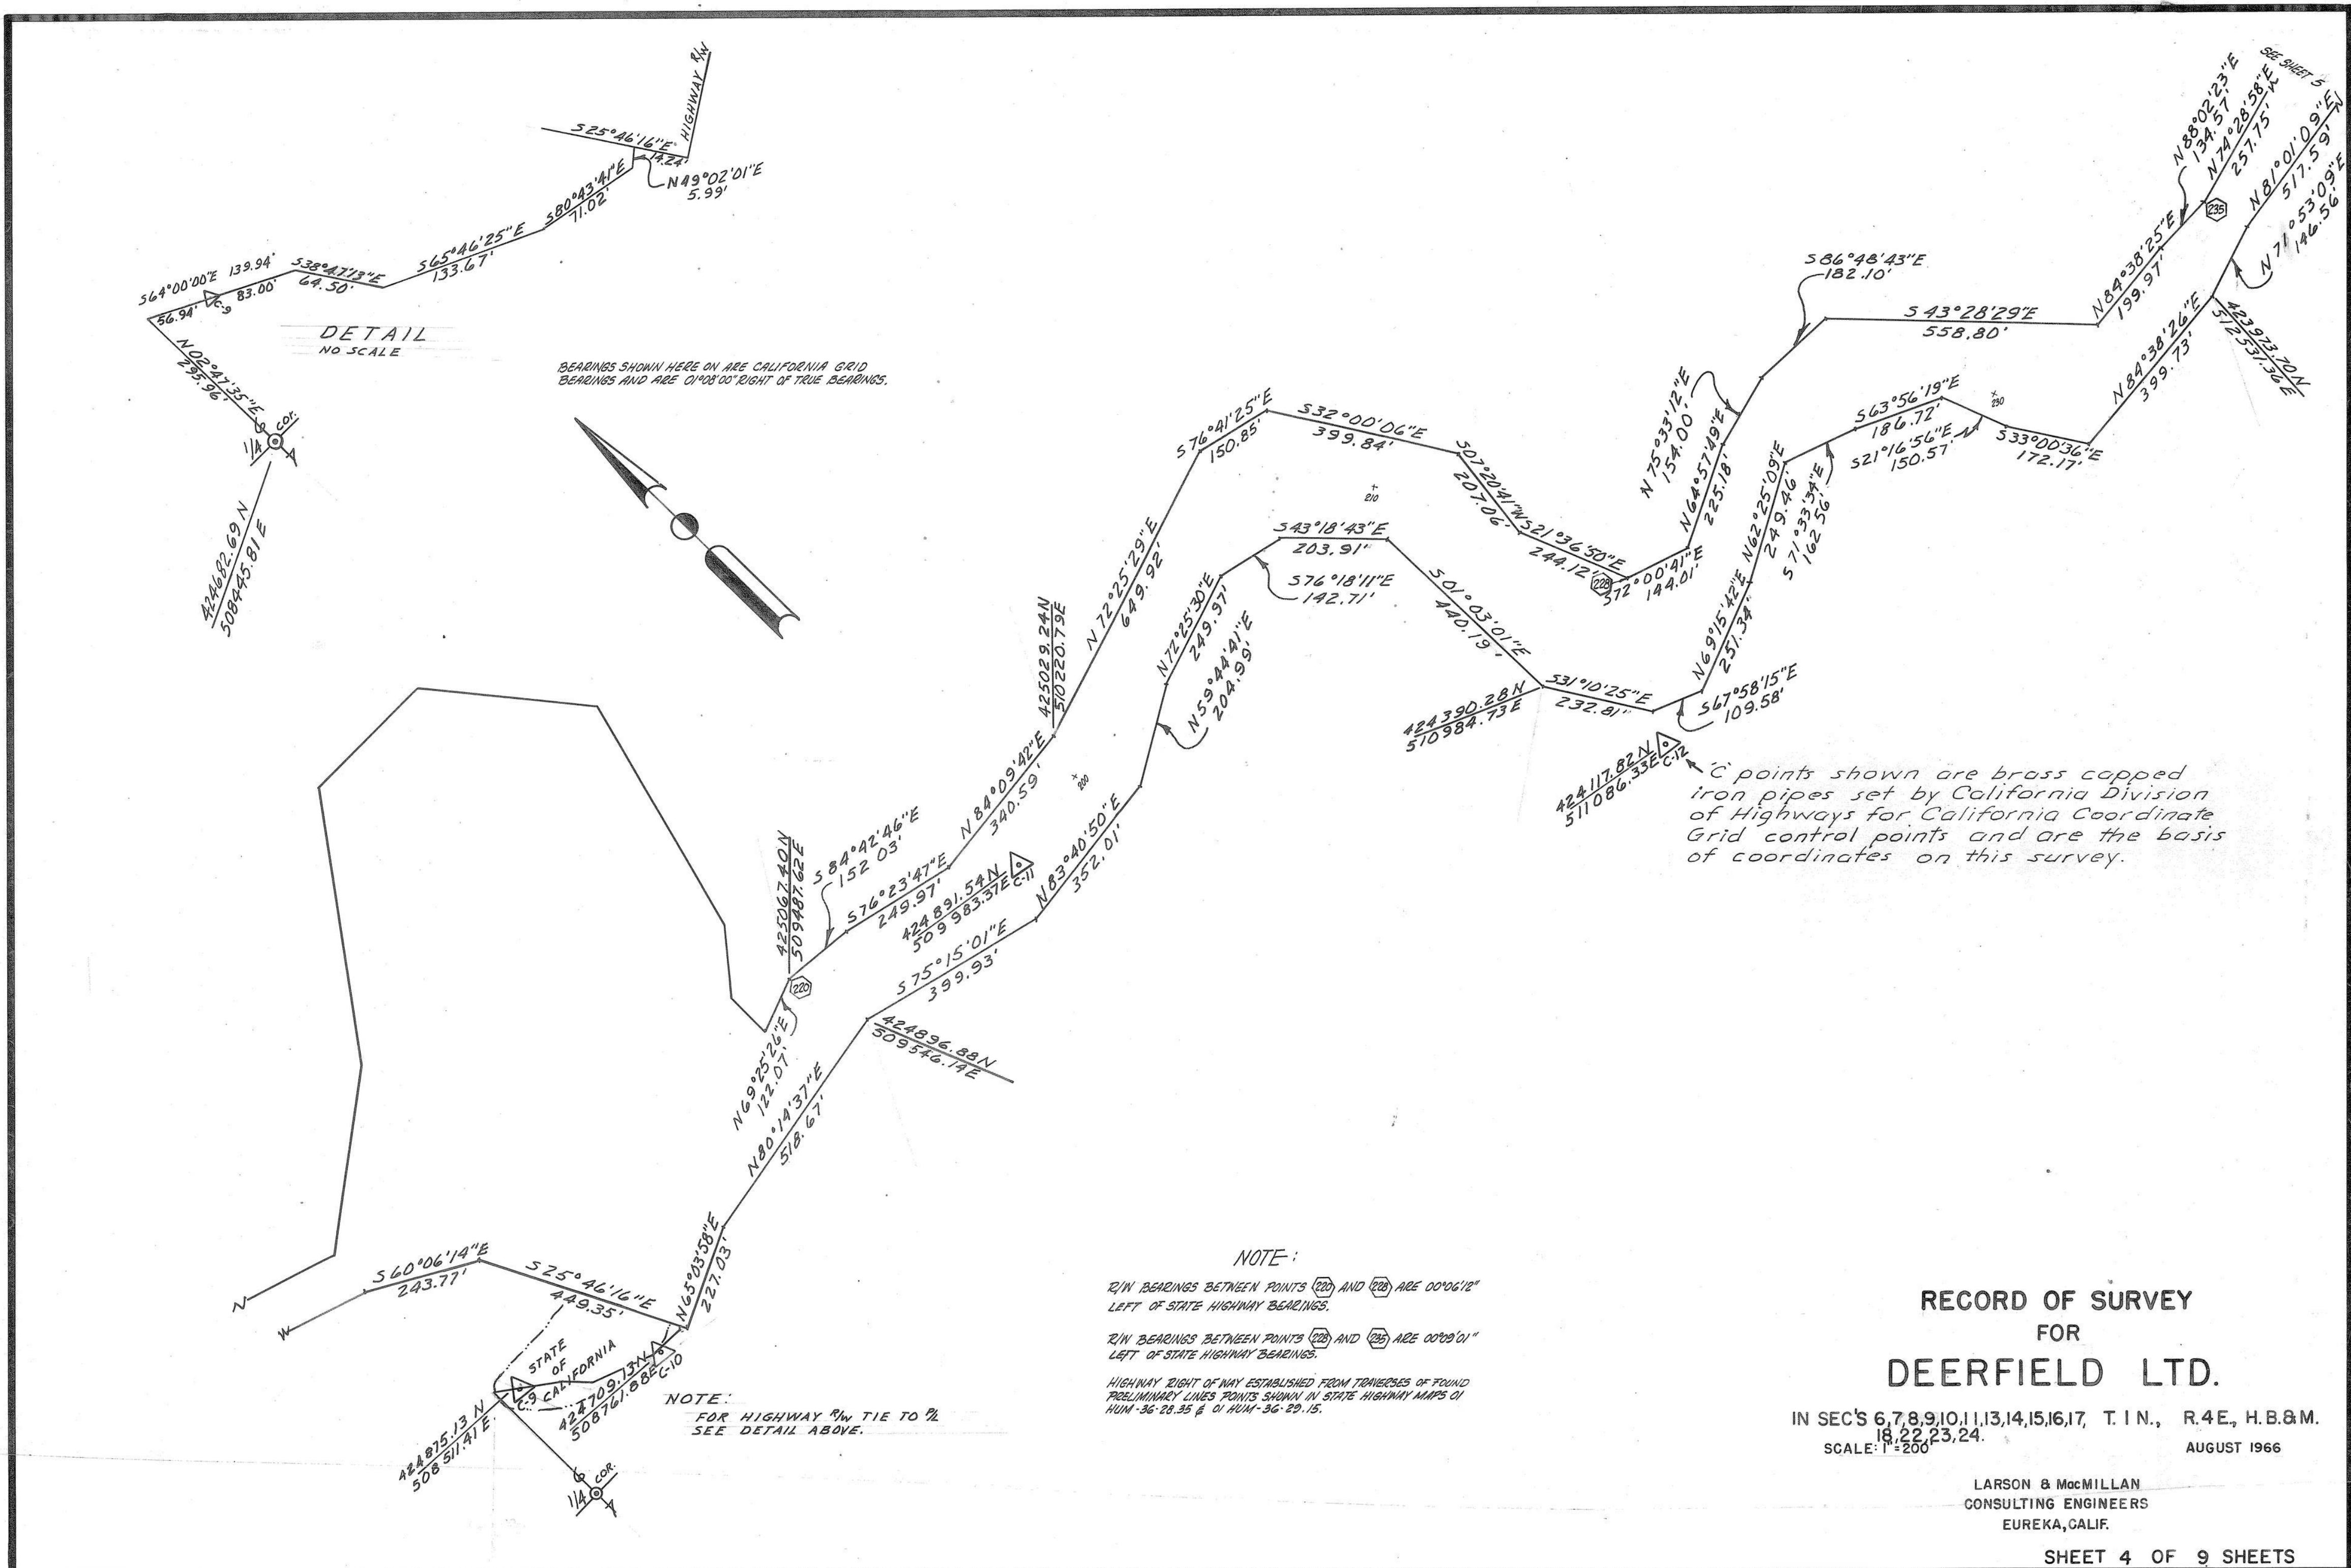

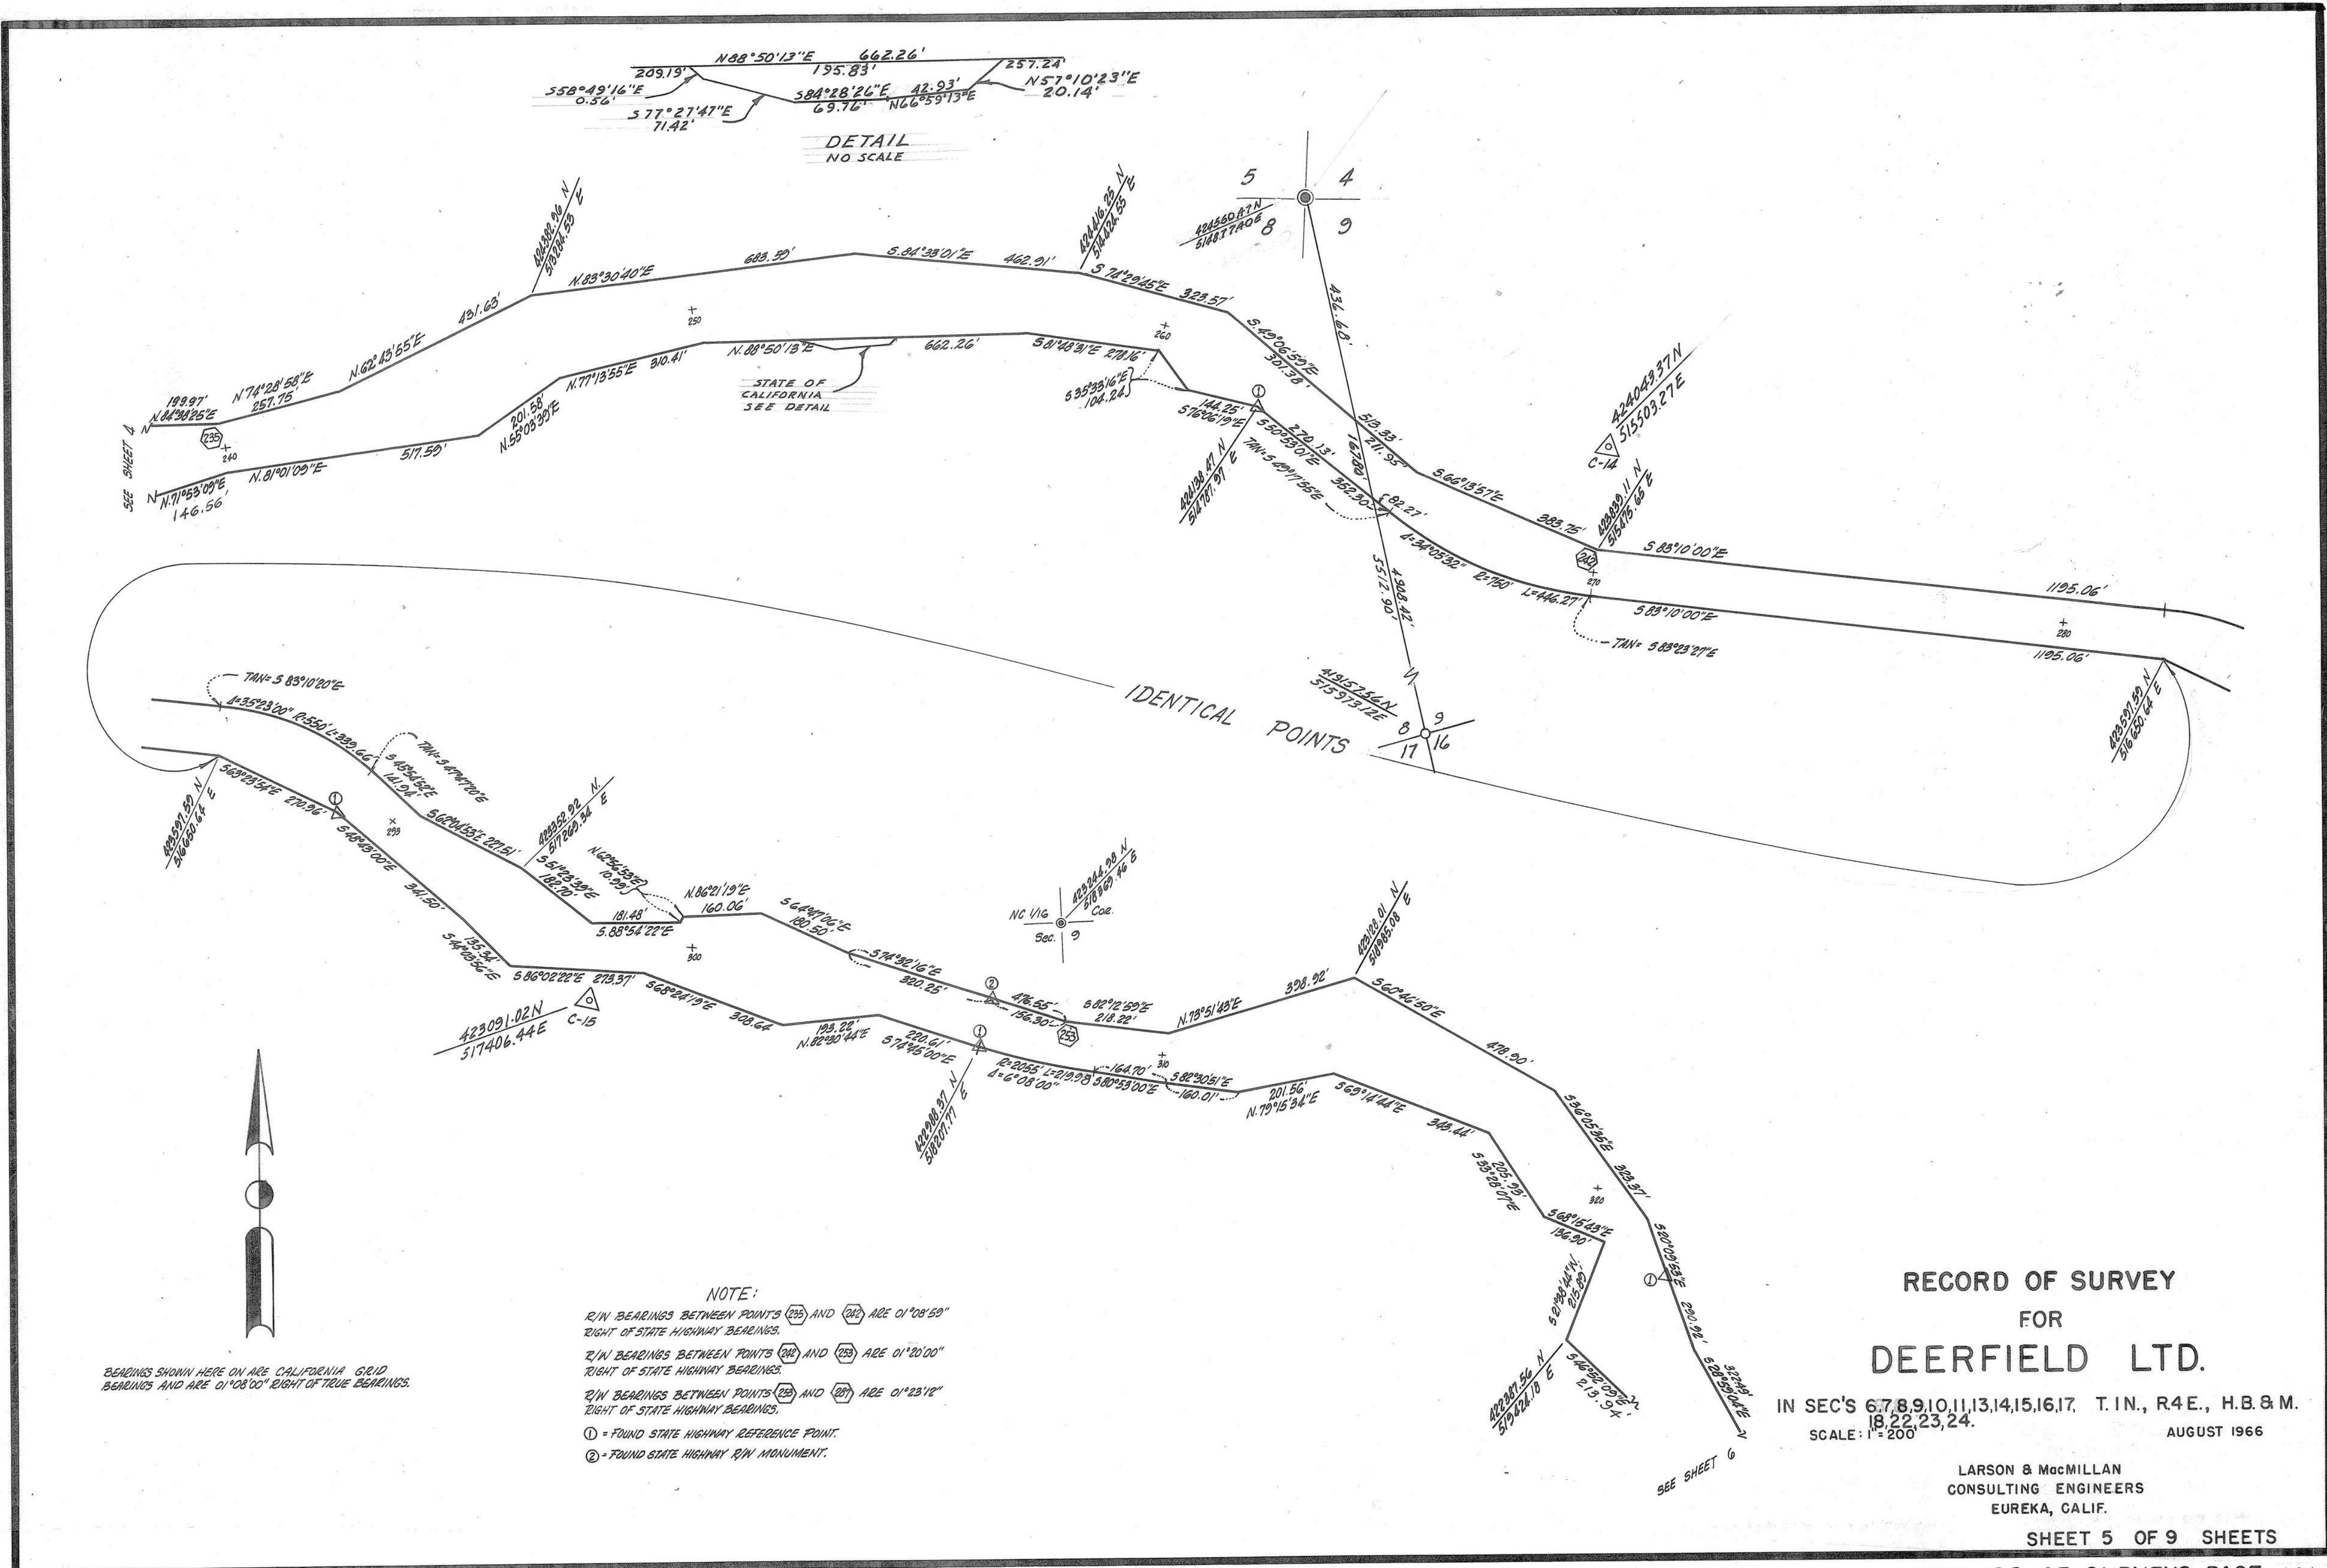

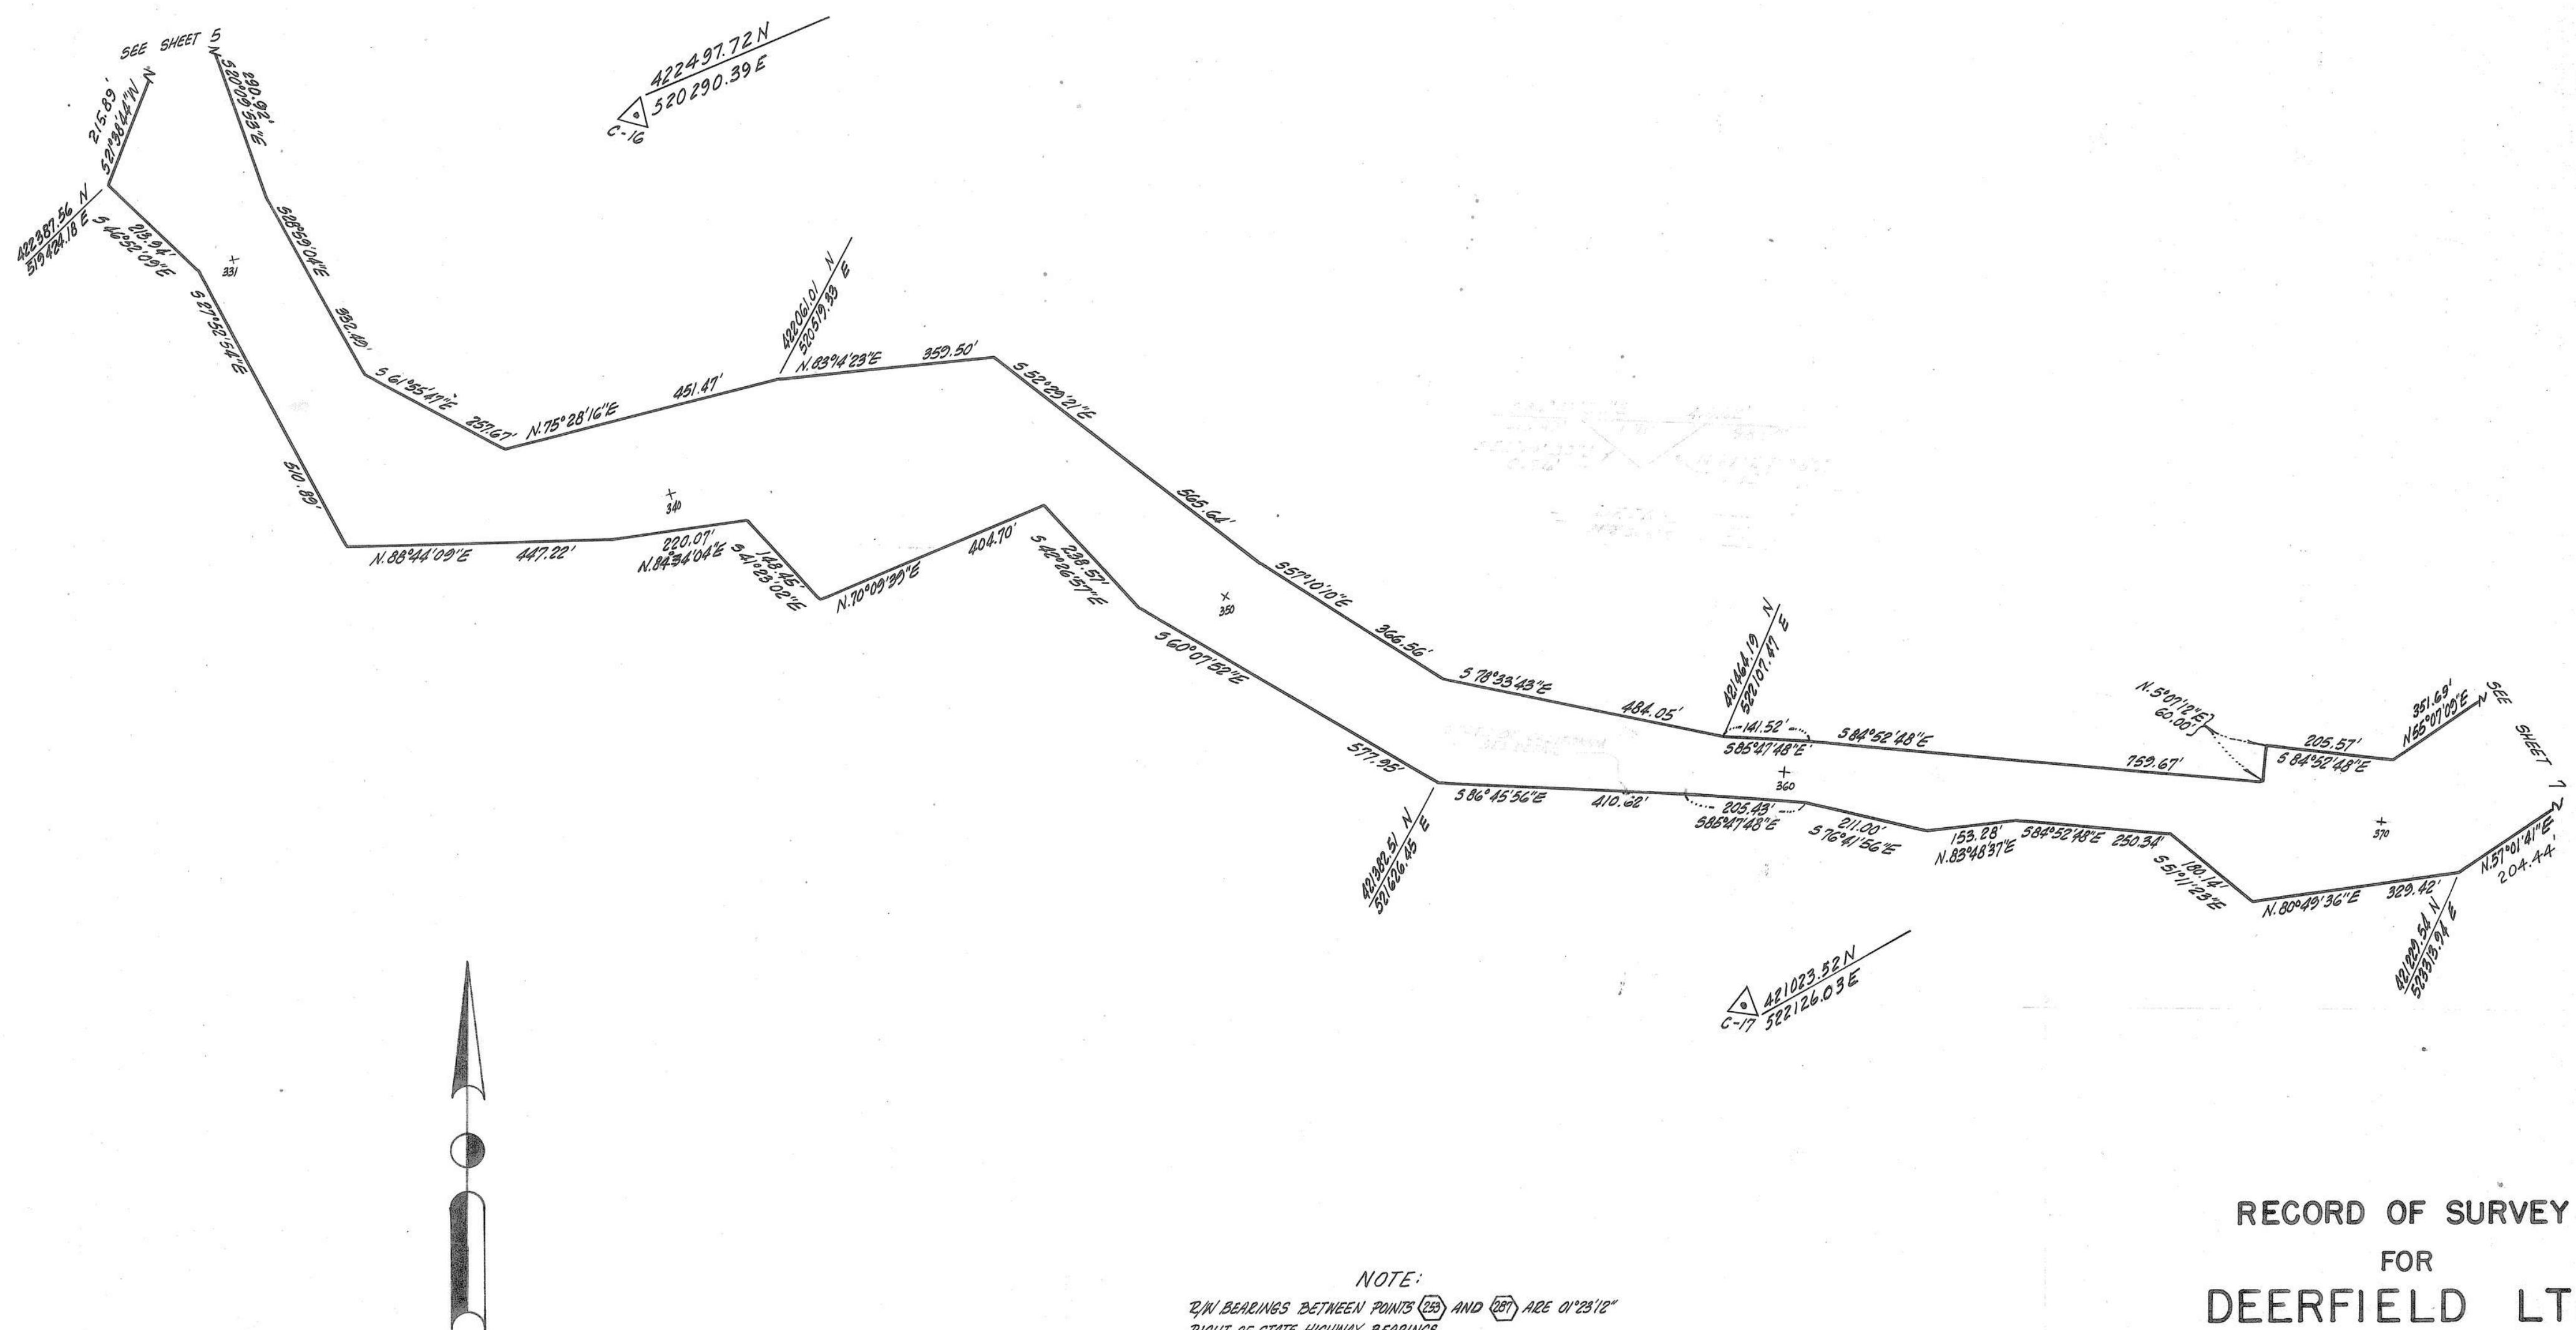

BEARINGS SHOWN HERE ON ARE CALIFORNIA GRID BEARINGS
AND ARE 01°08'00" RIGHT OF TRUE BEARINGS.


RECORD OF SURVEY
FOR
DEERFIELD LTD.

IN SEC'S 6,7,8,9,10,11,13,14,15,16,17, T.I.N., R. 4 E, H.B.&M.
18,22,23,24,
SCALE: 1 : 200
AUGUST 1966

LARSON & MacMILLAN
CONSULTING ENGINEERS
EUREKA, CALIF.

SHEET 6 OF 9 SHEETS

BOOK 22 OF SURVEYS, PAGE 102

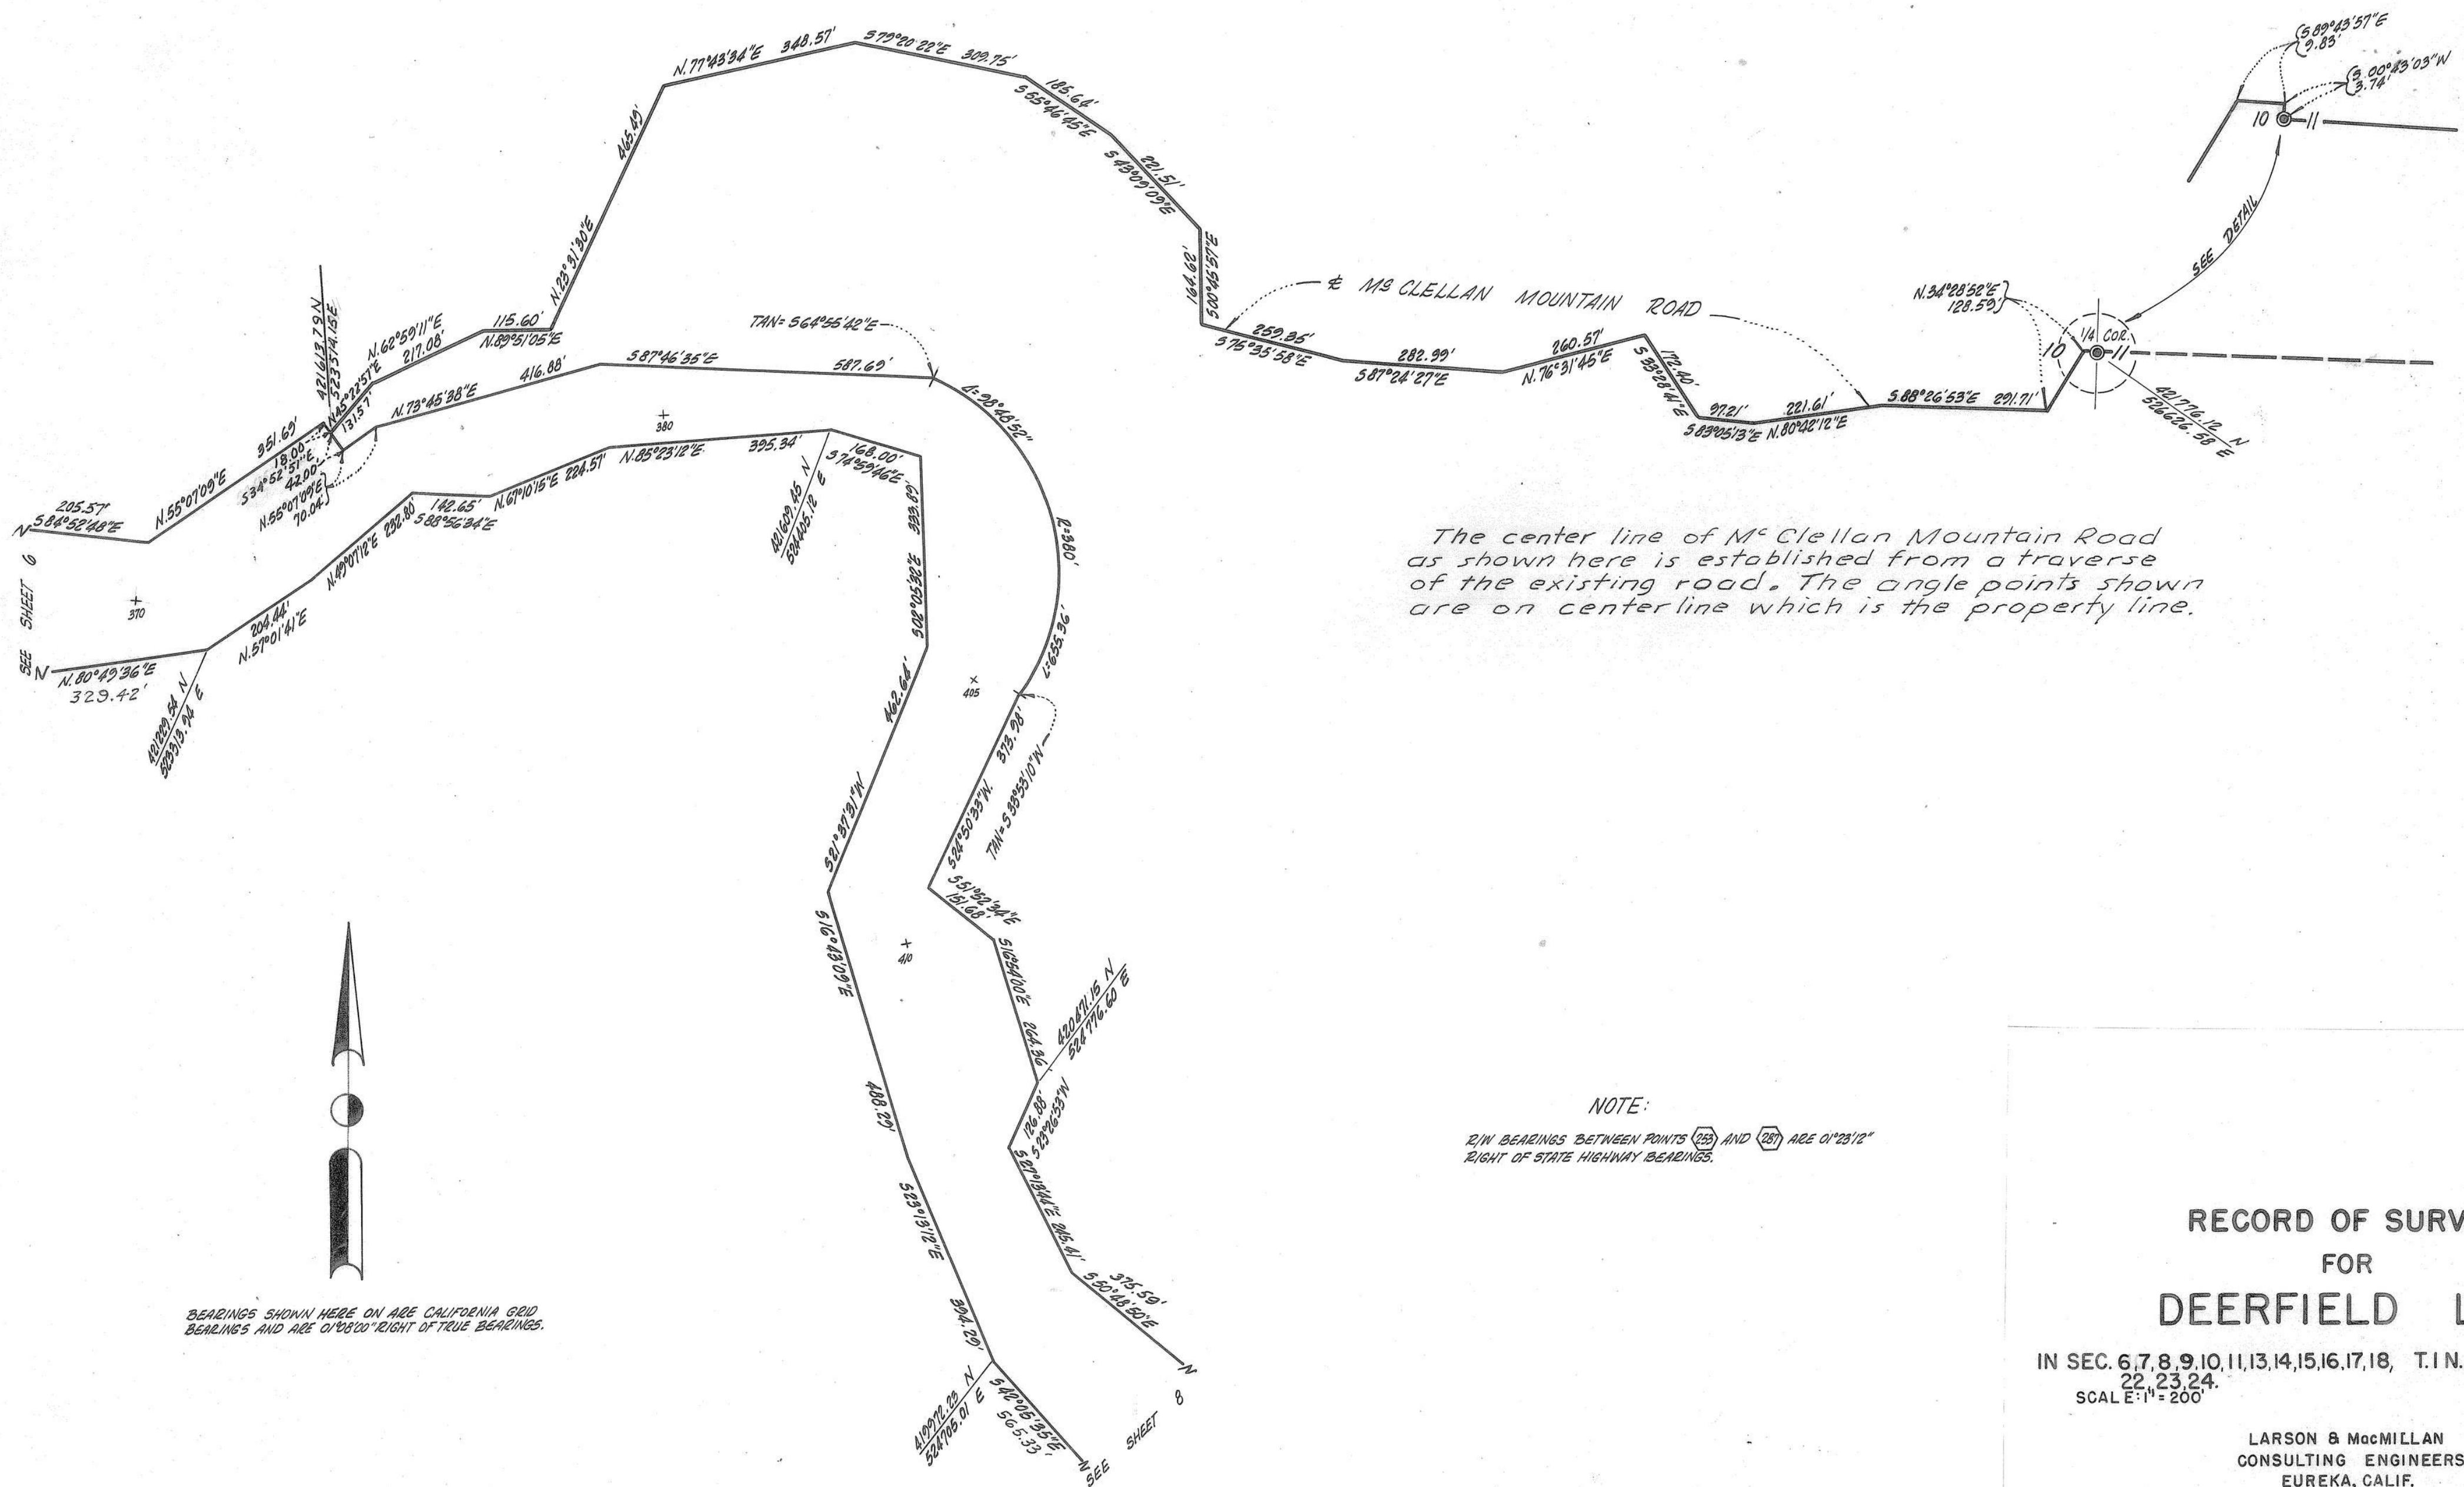

RECORD OF SURVEY FOR DEERFIELD LTD.


IN SEC. 6,7,8,9,10,11,13,14,15,16,17,18, T.I.N., R.4E., H.B.&M.
22 23 24.
SCALE E:1" = 200'


AUGUST 1966

LARSON & MacMILLAN
CONSULTING ENGINEERS
EUREKA, CALIF.

SHEET 7 OF 9 SHEETS

BOOK 22 OF SURVEYS, PAGE 103

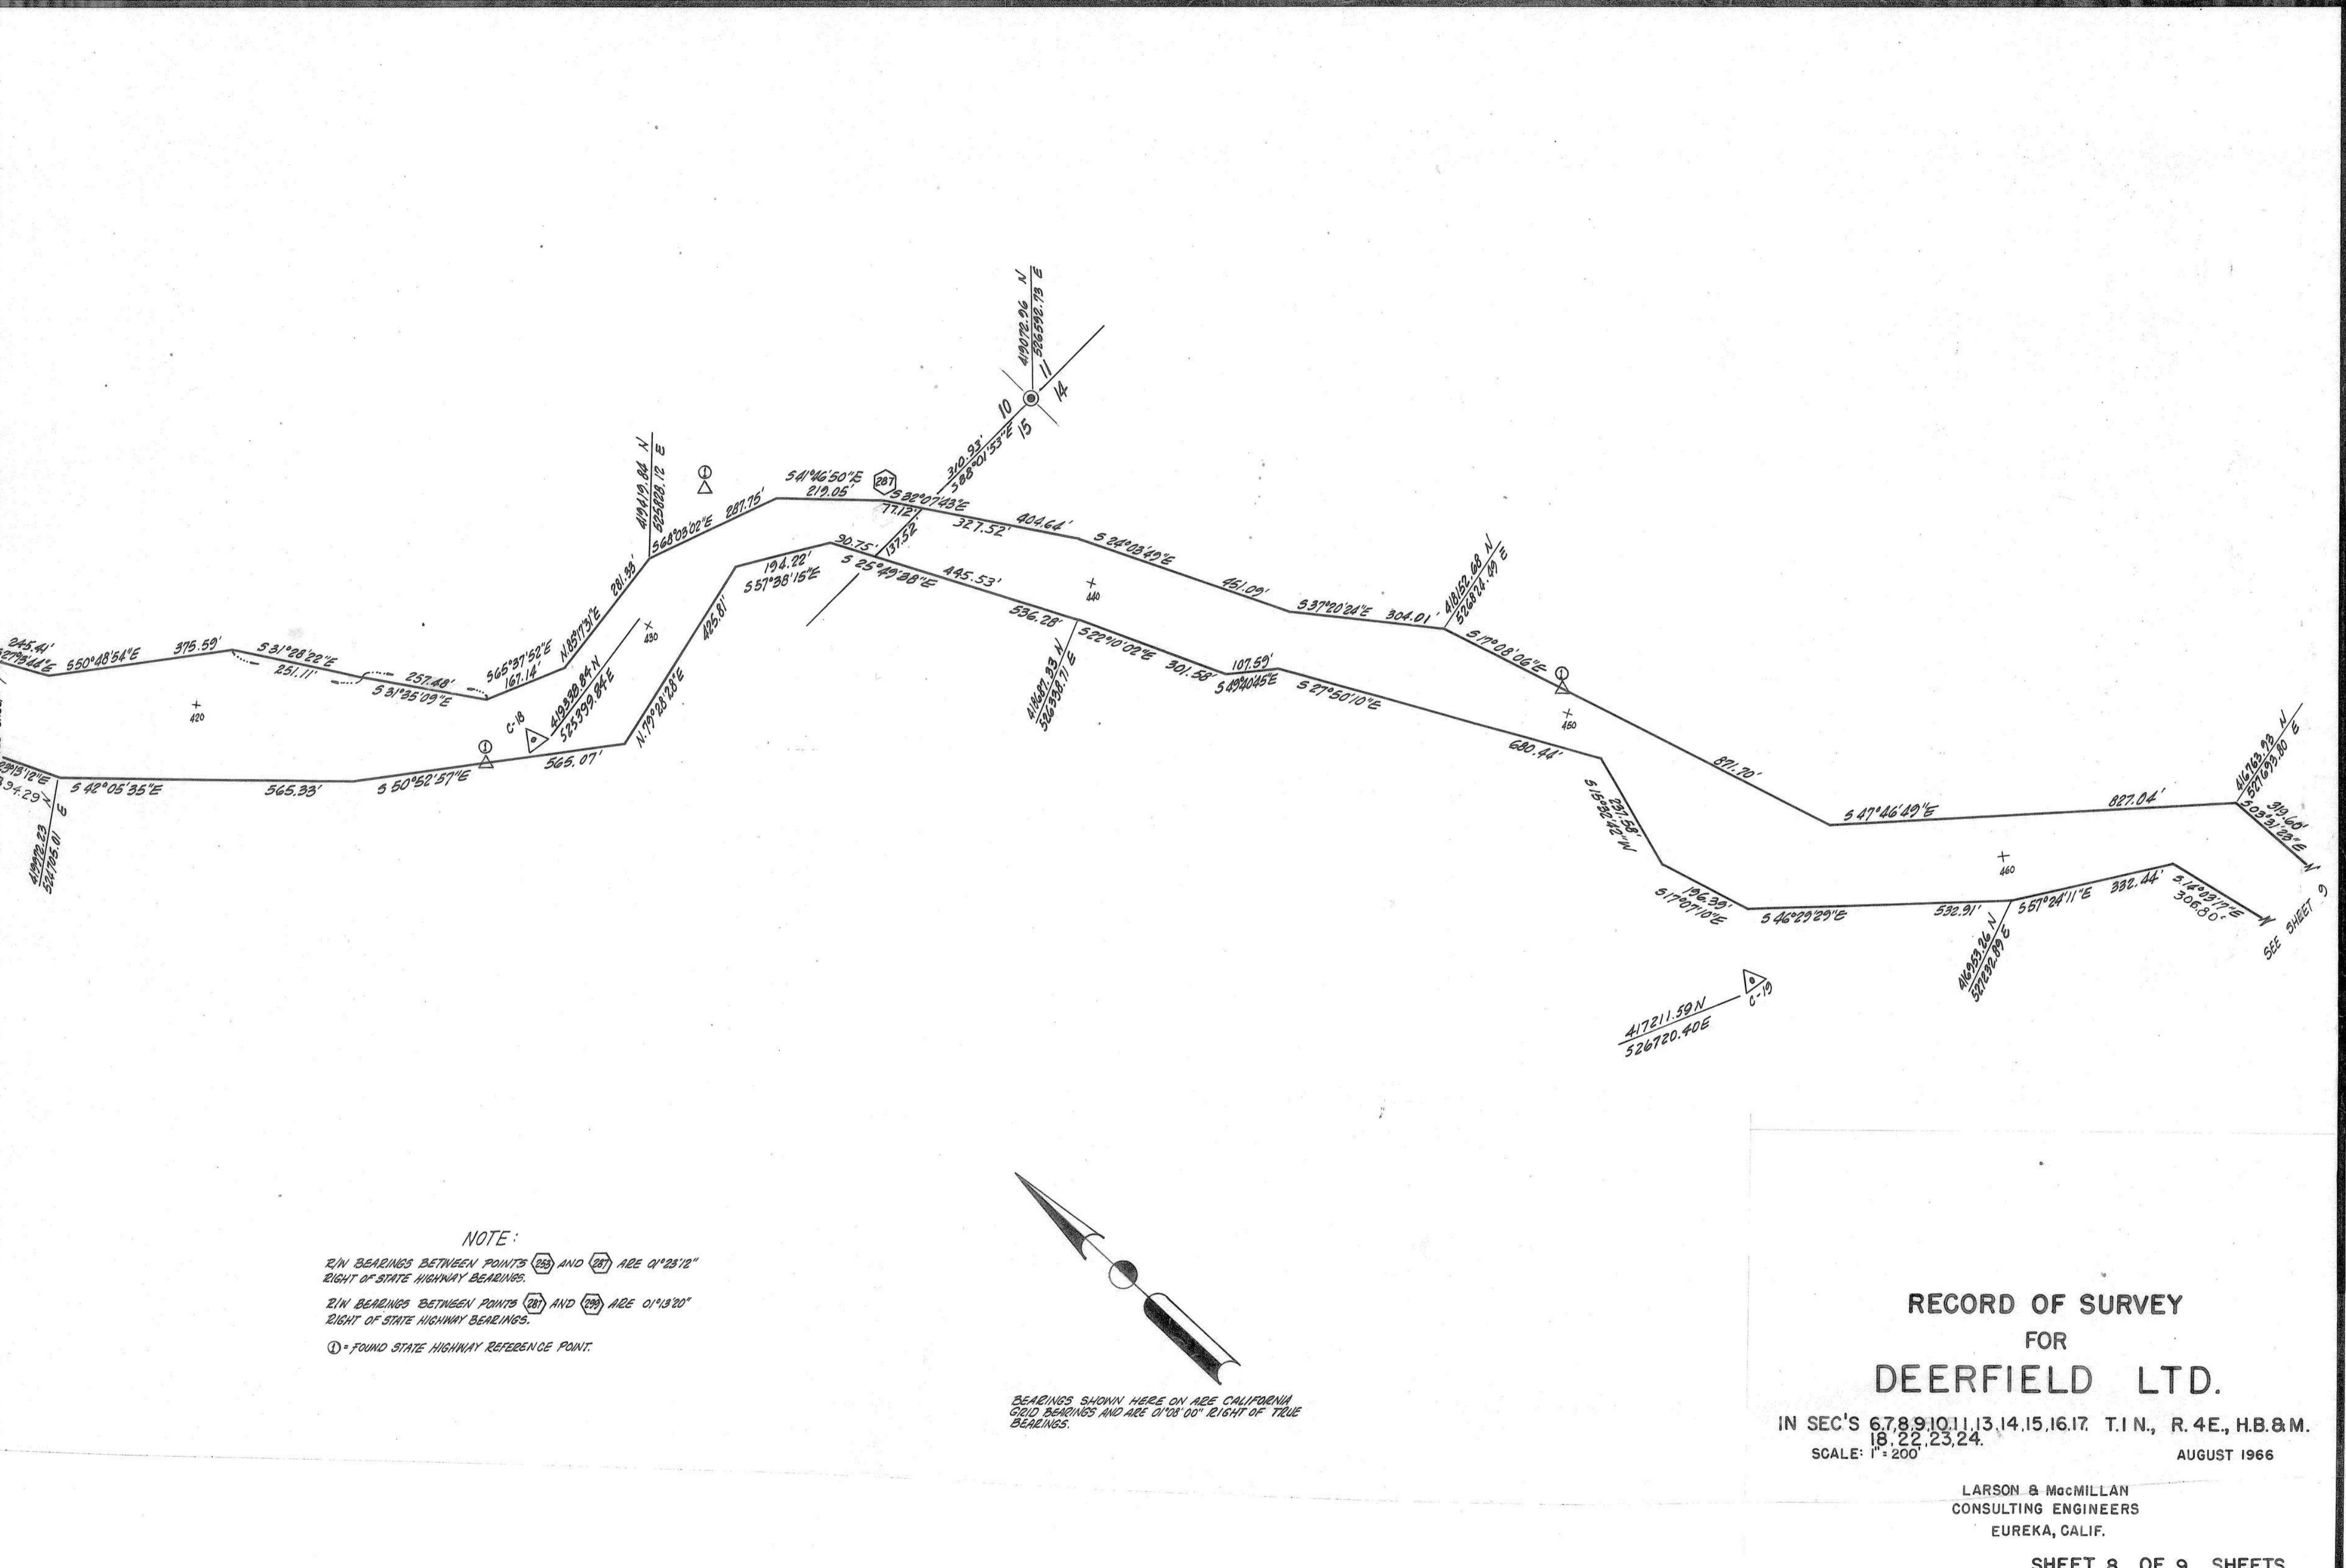

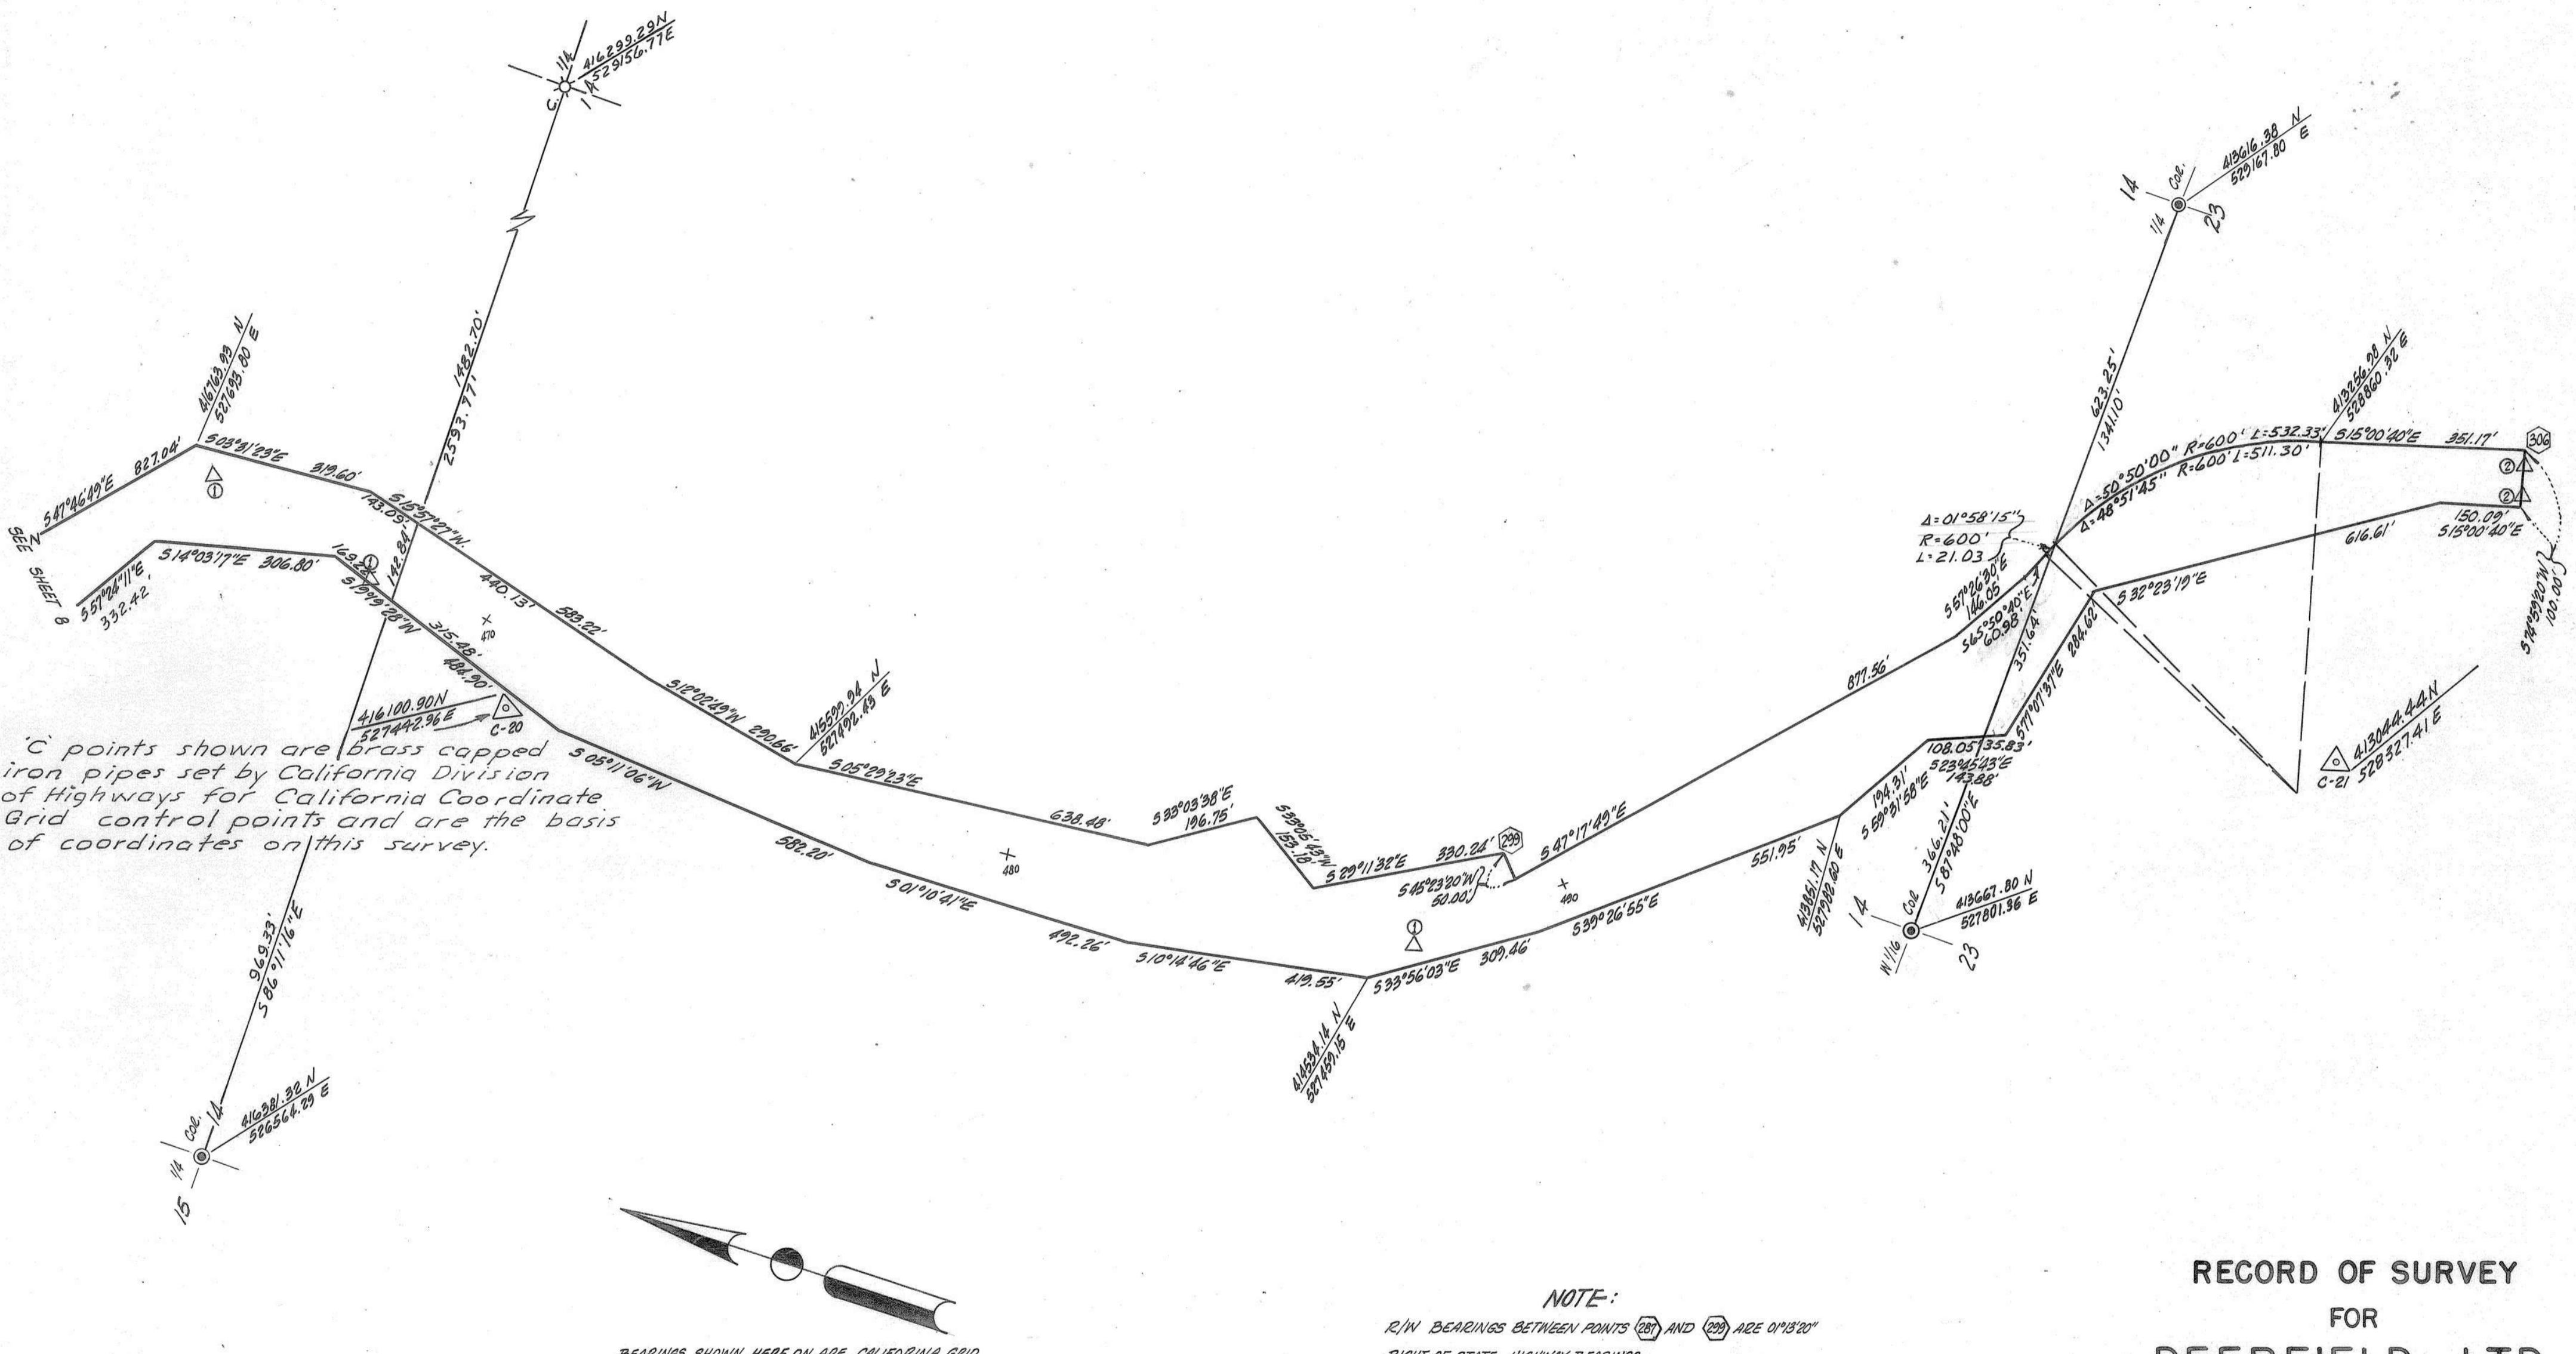

NOTE:

R/W BEARINGS BETWEEN POINTS ②81 AND ②89 ARE $01^{\circ} 8' 20''$ RIGHT OF STATE HIGHWAY BEARINGS.

R/W BEARINGS BETWEEN POINTS ②89 AND ②90 ARE $01^{\circ} 1' 20''$ RIGHT OF STATE HIGHWAY BEARINGS.

① = FOUND STATE HIGHWAY REFERENCE POINT.

② = FOUND STATE HIGHWAY R/W MONUMENT.

RECORD OF SURVEY FOR DEERFIELD LTD.

IN SEC'S 6, 7, 8, 9, 10, 11, 13, 14, 15, 16, 17, 18, T. I. N., R. 4 E., H. B. & M.
22, 23, 24.
SCALE: 1" = 200'

AUGUST 1966

LARSON & MacMILLAN
CONSULTING ENGINEERS
EUREKA, CALIF.

SHEET 9 OF 9 SHEETS